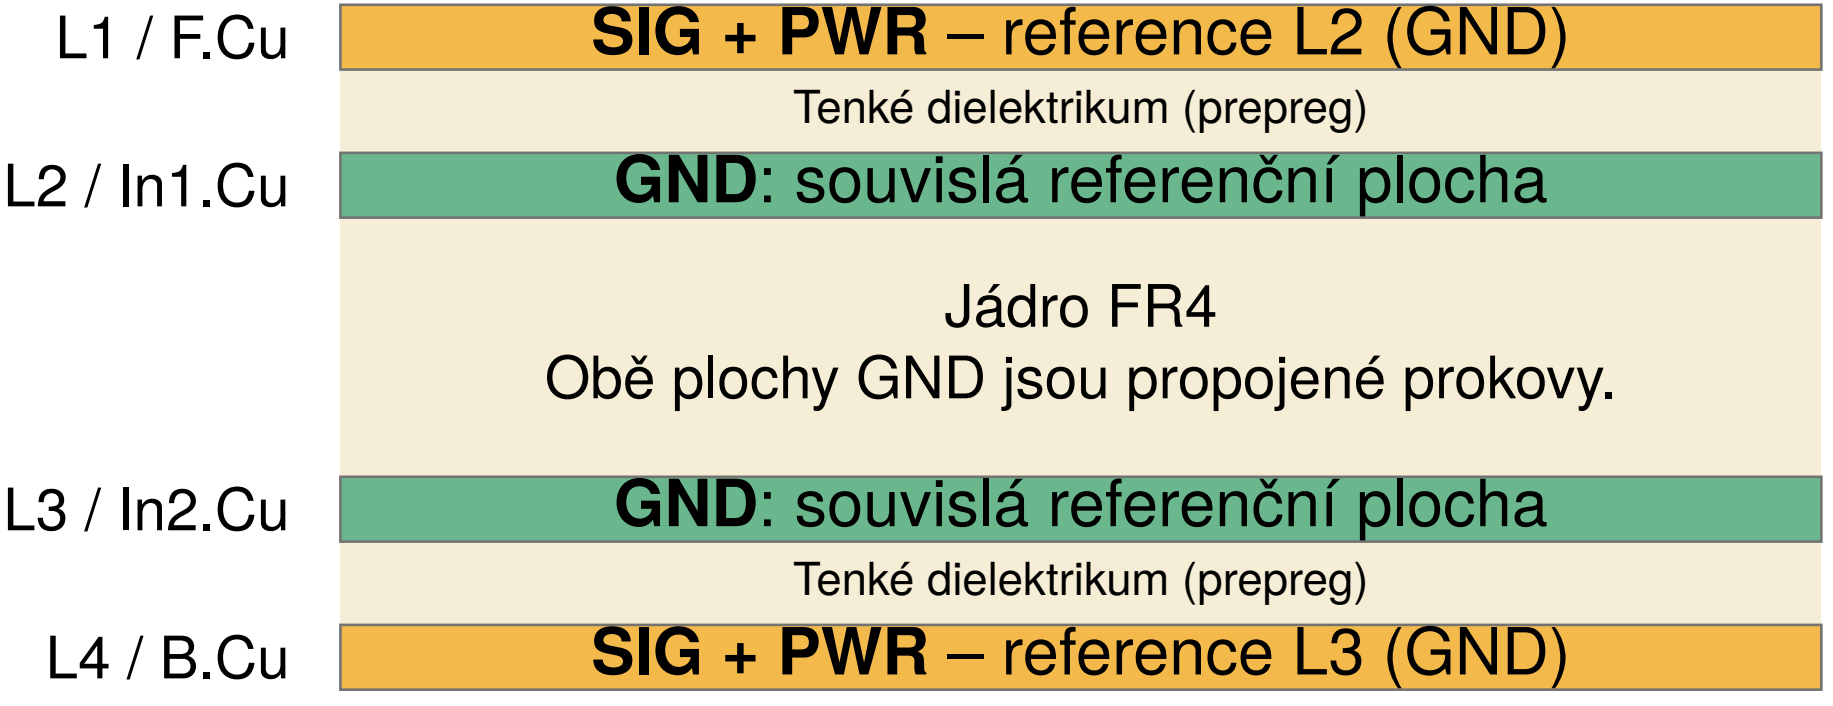

Schématický řez; napájení na vnějších vrstvách tvoří trasy nebo polygony.